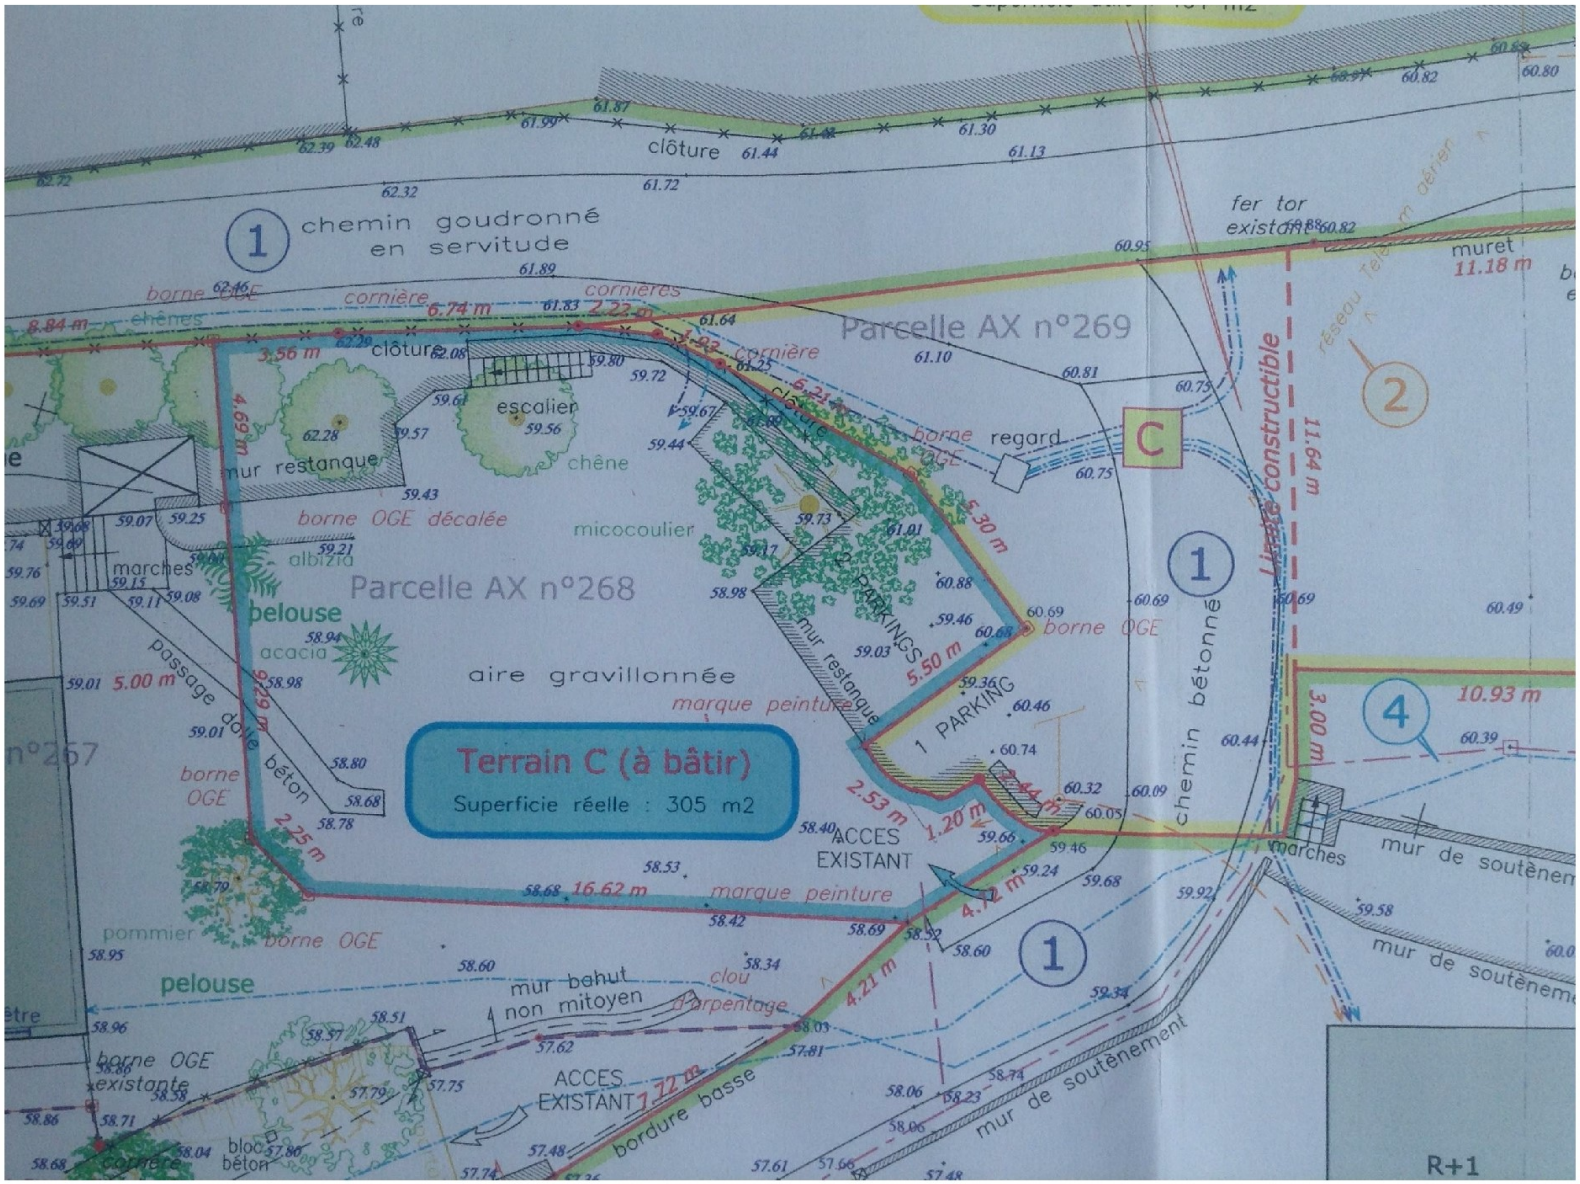


DPC

Réalisation d'une Maison individuelle

N°	Description	Date

Maître d'ouvrage
M.Mirales
12, rue du vent 13400 Miramas.

Projet :
Réalisation d'une maison individuelle
Lieu dit Provence à 13100 Grans

PCMI


Numéro du projet	V1
Date	Janvier 2016
Dessiné par	M.Architecte


Plan géomètre

Echelle *Sans echelle*

08/08/2016 11:44:29



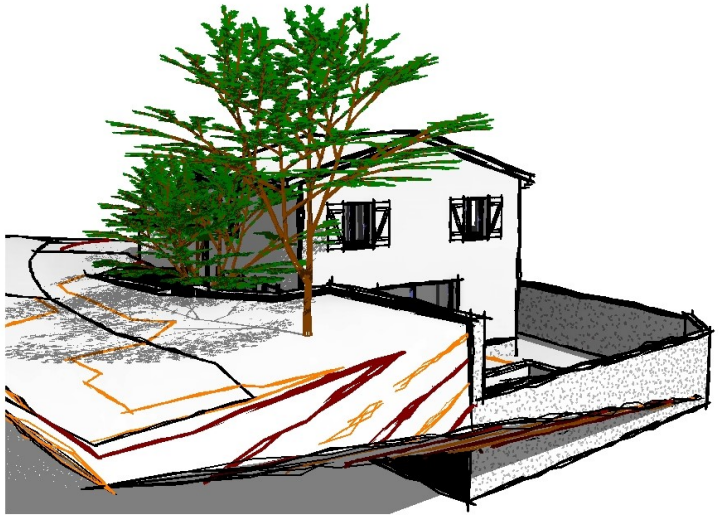

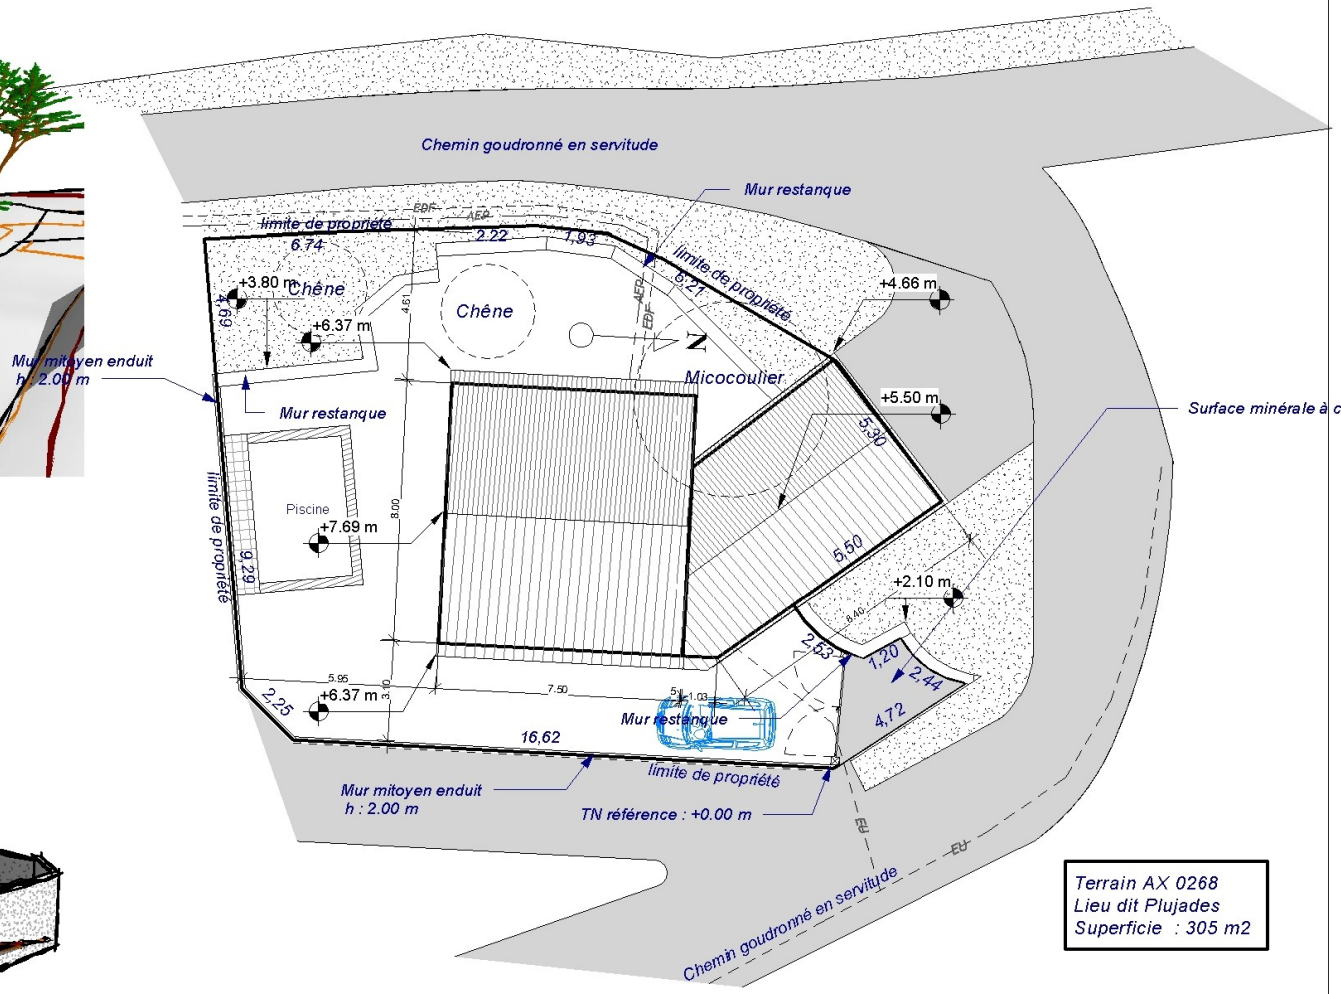

DPC

Réalisation d'une Maison individuelle

N°	Description	Date

Maître d'ouvrage
M.Mirales
12, rue du vent 13400 Miramas.

Projet :
Réalisation d'une maison individuelle
Lieu dit Provence à 13100 Grans


PCMI 2


Numéro du projet	V1
Date	Janvier 2016
Dessiné par	M.Architecte

Plan de Masse

Echelle 1 : 150

08/08/2016 11:47:51

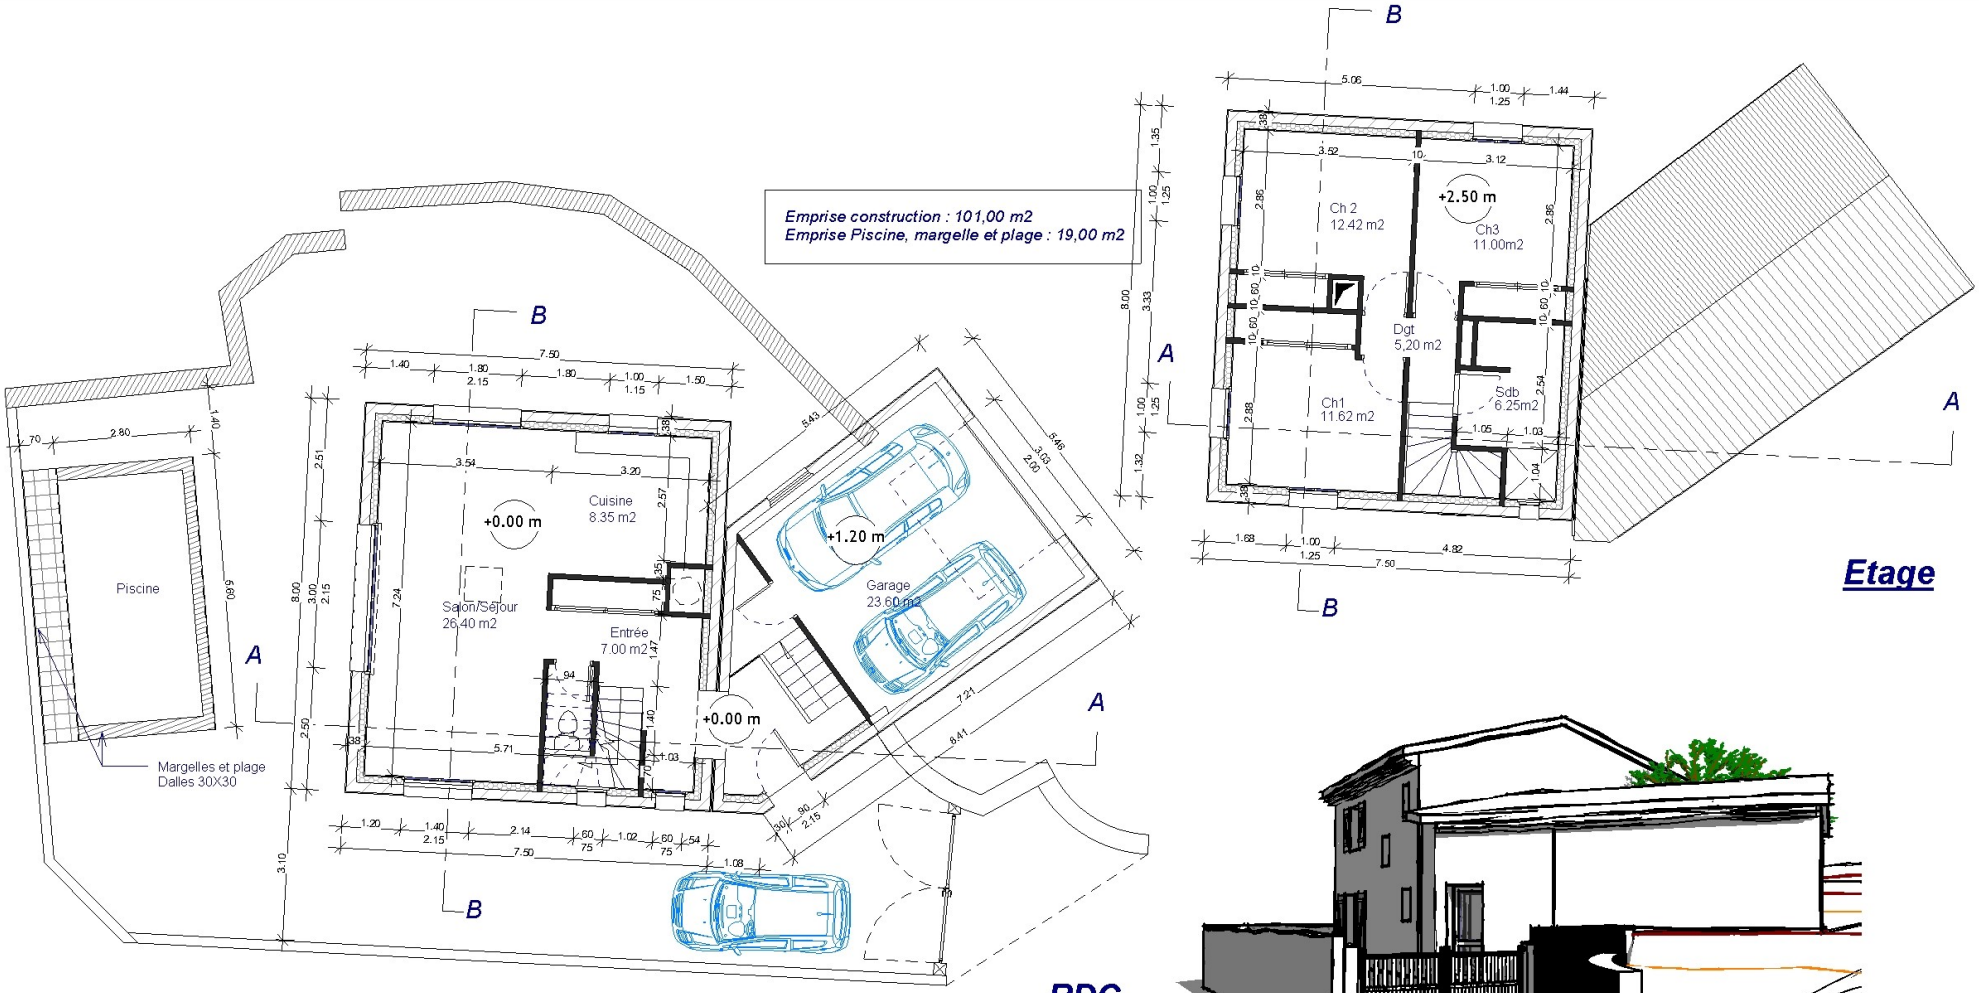

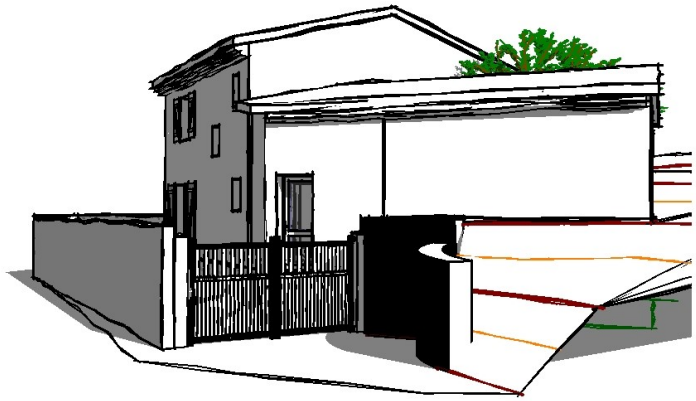

DPC

Réalisation d'une Maison individuelle

N°	Description	Date

Maître d'ouvrage
M.Mirales
12, rue du vent 13400 Miramas.


Projet :
Réalisation d'une maison individuelle
Lieu dit Provence à 13100 Grans

PCMI

Numéro du projet	V1
Date	Janvier 2016
Dessiné par	M.Architecte
Echelle	1 : 100

Plans

08/08/2016 11:44:01

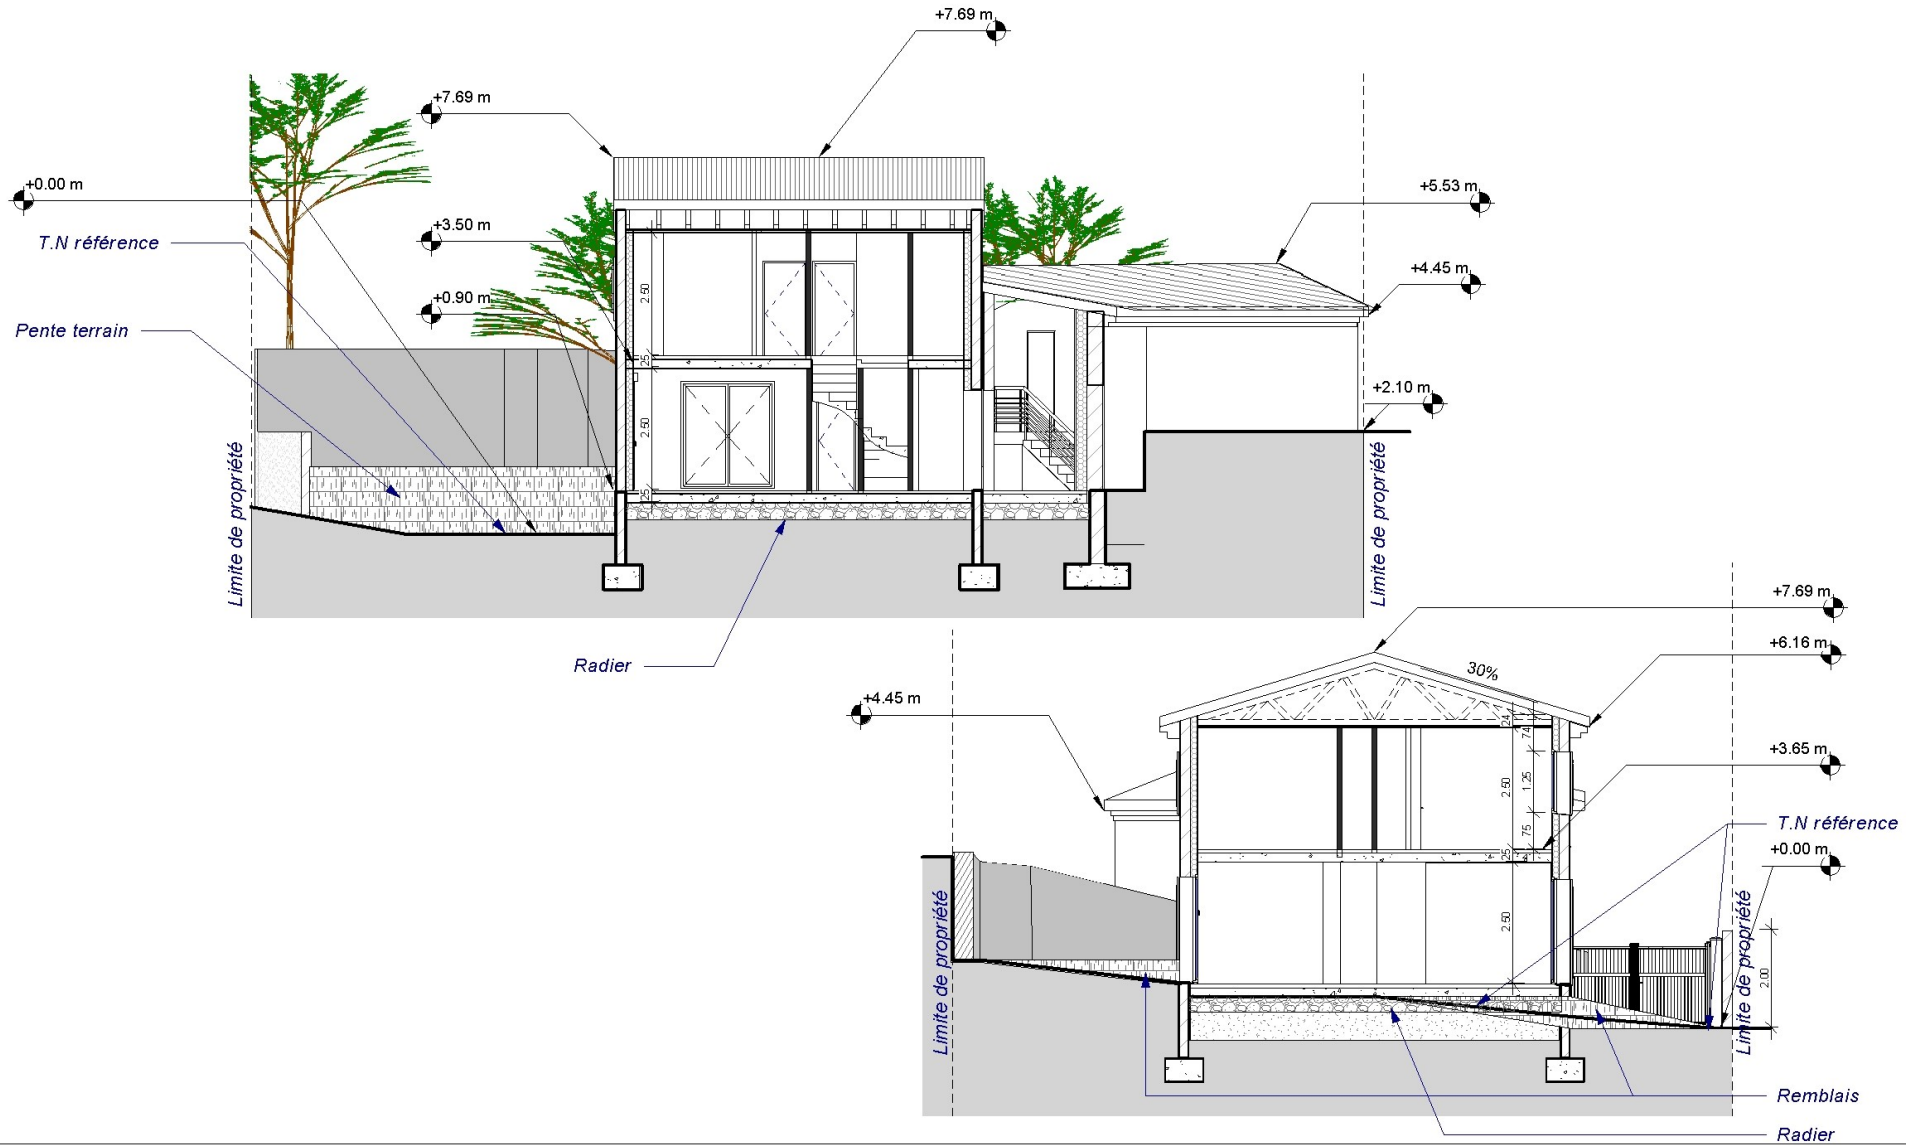

DPC

Réalisation d'une Maison individuelle

N°	Description	Date

Maître d'ouvrage
M.Mirales
12, rue du vent 13400 Miramas.

Projet :
Réalisation d'une maison individuelle
Lieu dit Provence à 13100 Grans


PCMI 3

Numéro du projet	V1
Date	Janvier 2016
Dessiné par	M.Architecte

Coupes

Echelle 1 : 100


08/08/2016 11:52:51

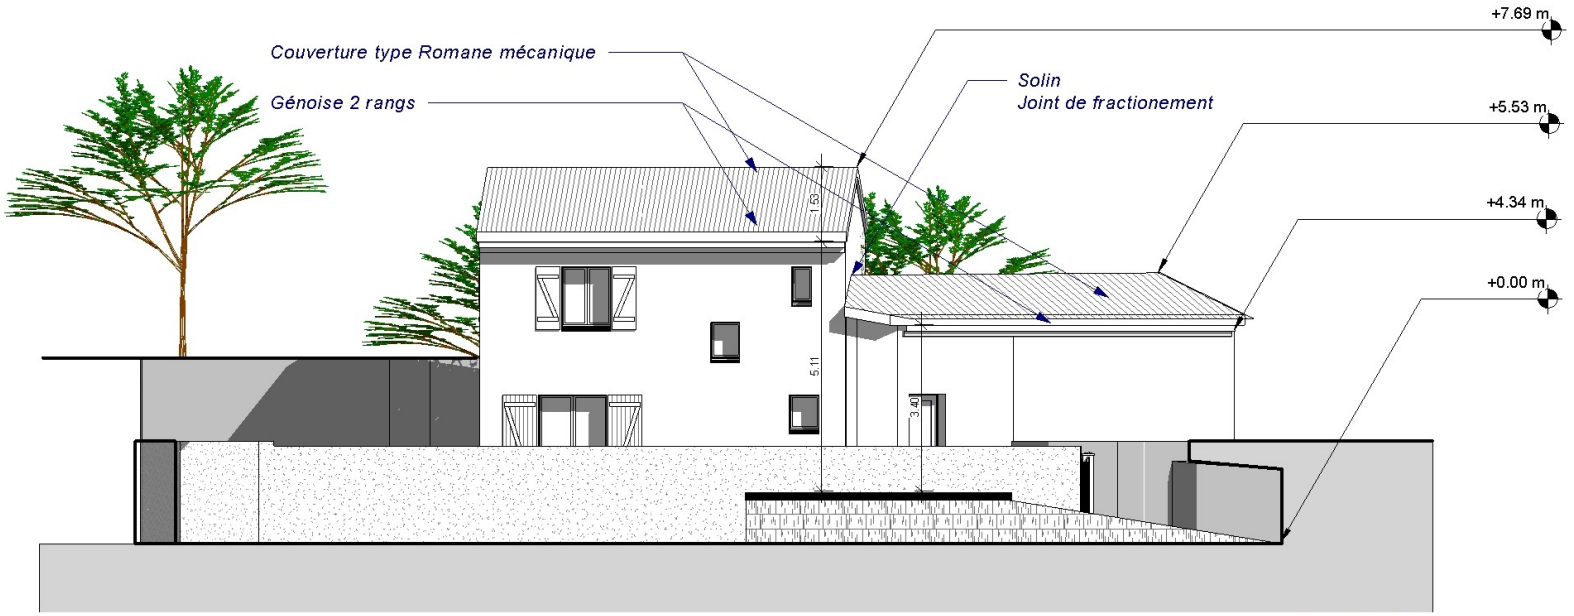

Façade Est



Façade Nord

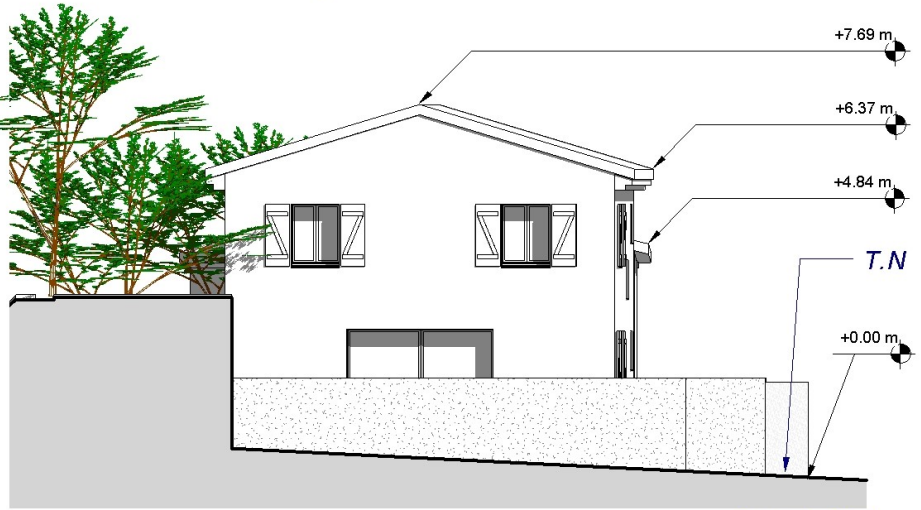

Façade Sud

DPC

Réalisation d'une Maison individuelle

N°	Description	Date

Maître d'ouvrage
M.Mirales
12, rue du vent 13400 Miramas.

Projet :
Réalisation d'une maison individuelle
Lieu dit Provence à 13100 Grans


PCMI 5

Numéro du projet	V1
Date	Janvier 2016
Dessiné par	M.Architecte
Echelle	1 : 100

Façades

08/08/2016 11:49:03



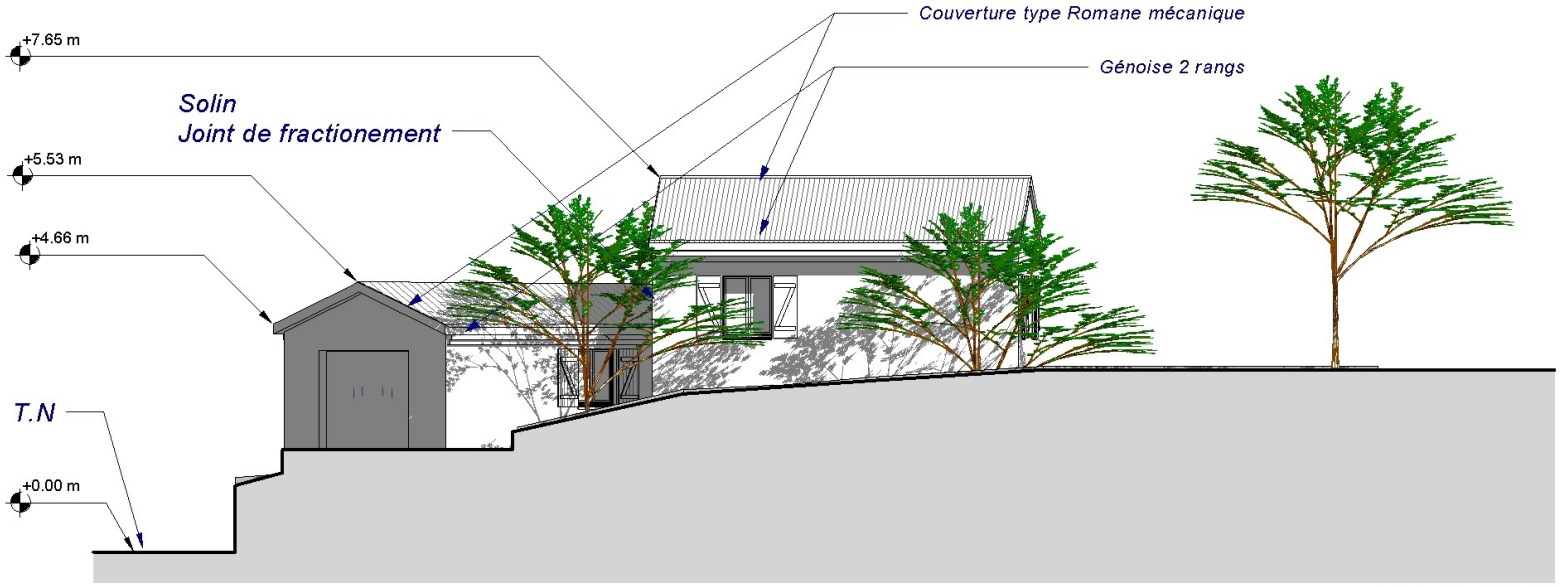

Façade Ouest

DPC

Réalisation d'une Maison individuelle

N°	Description	Date

Maître d'ouvrage
M.Mirales
12, rue du vent 13400 Miramas.

Projet :
Réalisation d'une maison individuelle
Lieu dit Provence à 13100 Grans

PCMI 5

Numéro du projet	V1
Date	Janvier 2016
Dessiné par	M.Architecte

Façade

Echelle 1 : 100

08/08/2016 11:52:20




PCMI 6



PCMI 8



PCMI 7

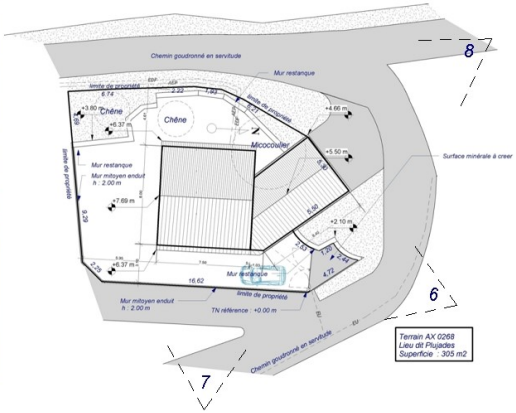

DPC

Réalisation d'une Maison individuelle

N°	Description	Date

Maître d'ouvrage
M.Mirales
12, rue du vent 13400 Miramas.

Projet :
Réalisation d'une maison individuelle
Lieu dit Provence à 13100 Grans

PCMI 6, 7, 8

Numéro du projet	V1
Date	Janvier 2016
Dessiné par	M.Architecte
Echelle	Pers

08/08/2016 11:48:21