Ville de Toulouse



Dossier Permis de Construire

Réalisation d'une Maison individuelle

Maître d'ouvrage


Sans nom

Numéro du projet	V1
Date	Juin 2016
Dessiné par	

Cartouche

Echelle

08/08/2016 11:22:10

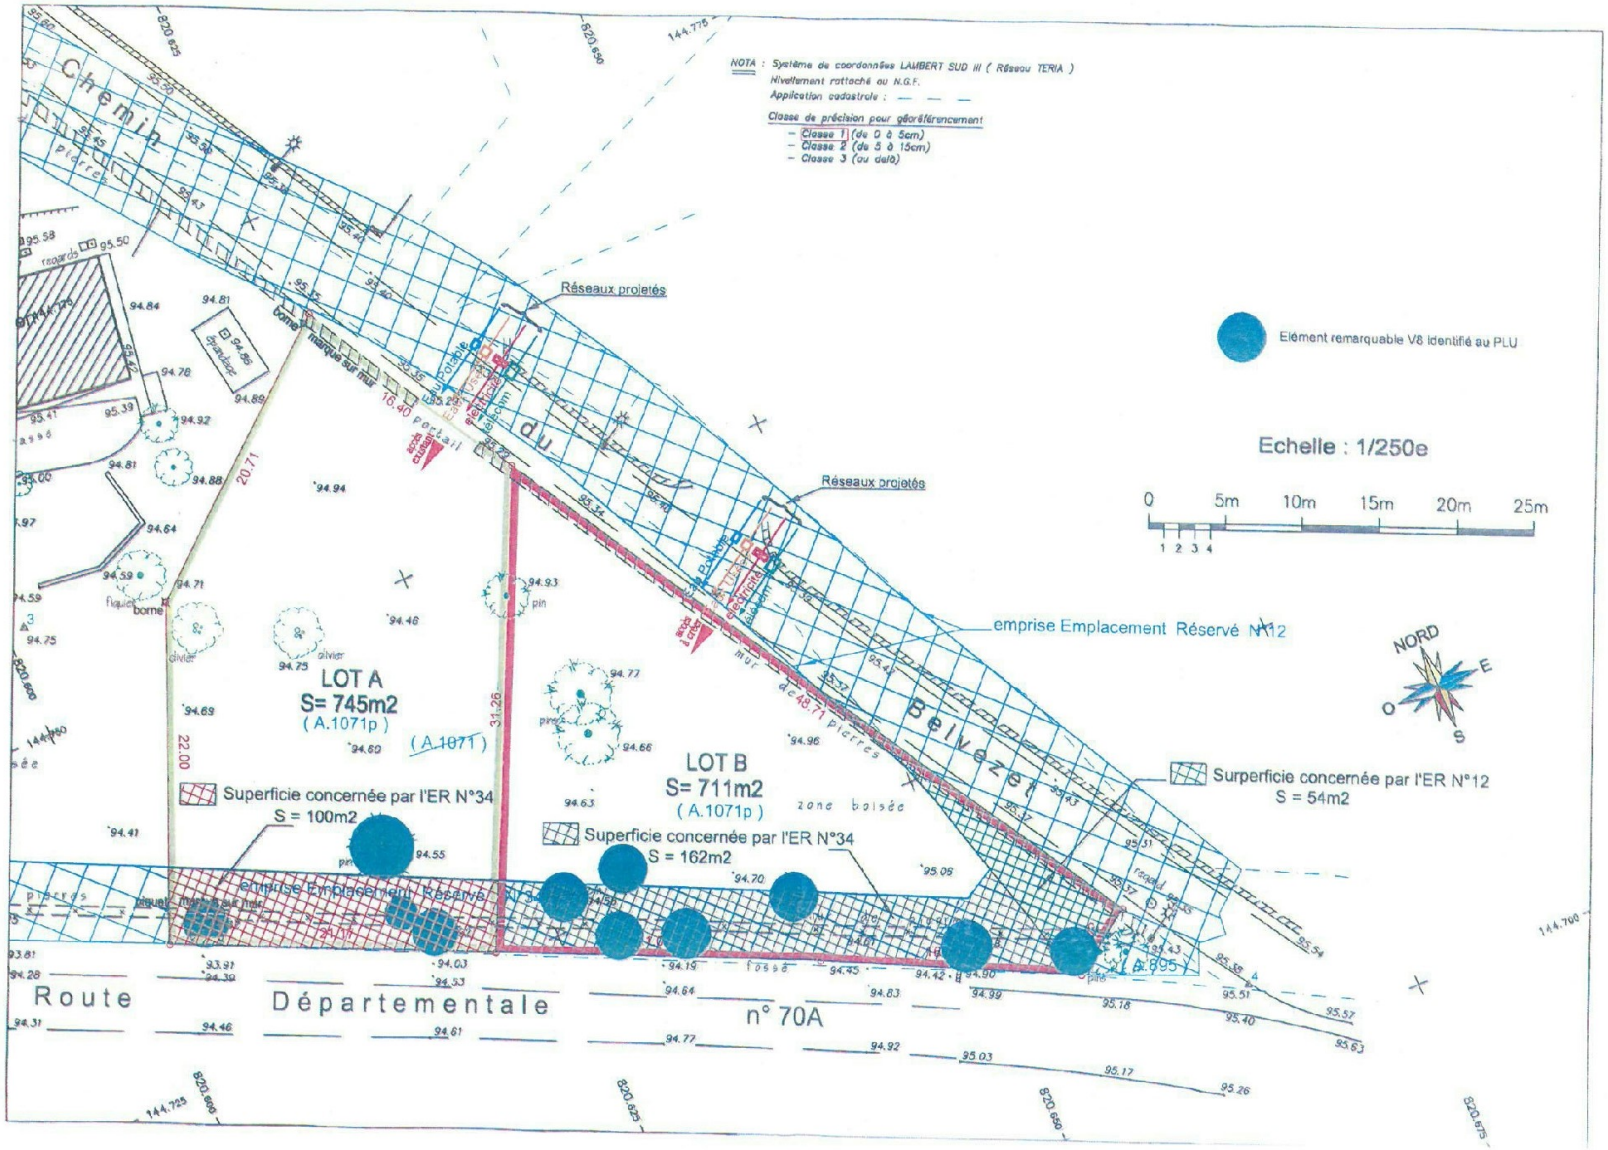

DPC

Réalisation d'une Maison individuelle

N°	Description	Date


Maître d'ouvrage
M.Bose
10, Rue Deners 31000 Toulouse
06.13.24.46.56
Projet :
12, chemin du Trigan
31300 Toulouse

PCMI

Numéro du projet	V1
Date	Juin 2016
Dessiné par	M.Architecte
Echelle	1/250°

Plan géomètre

08/08/2016 11:25:32

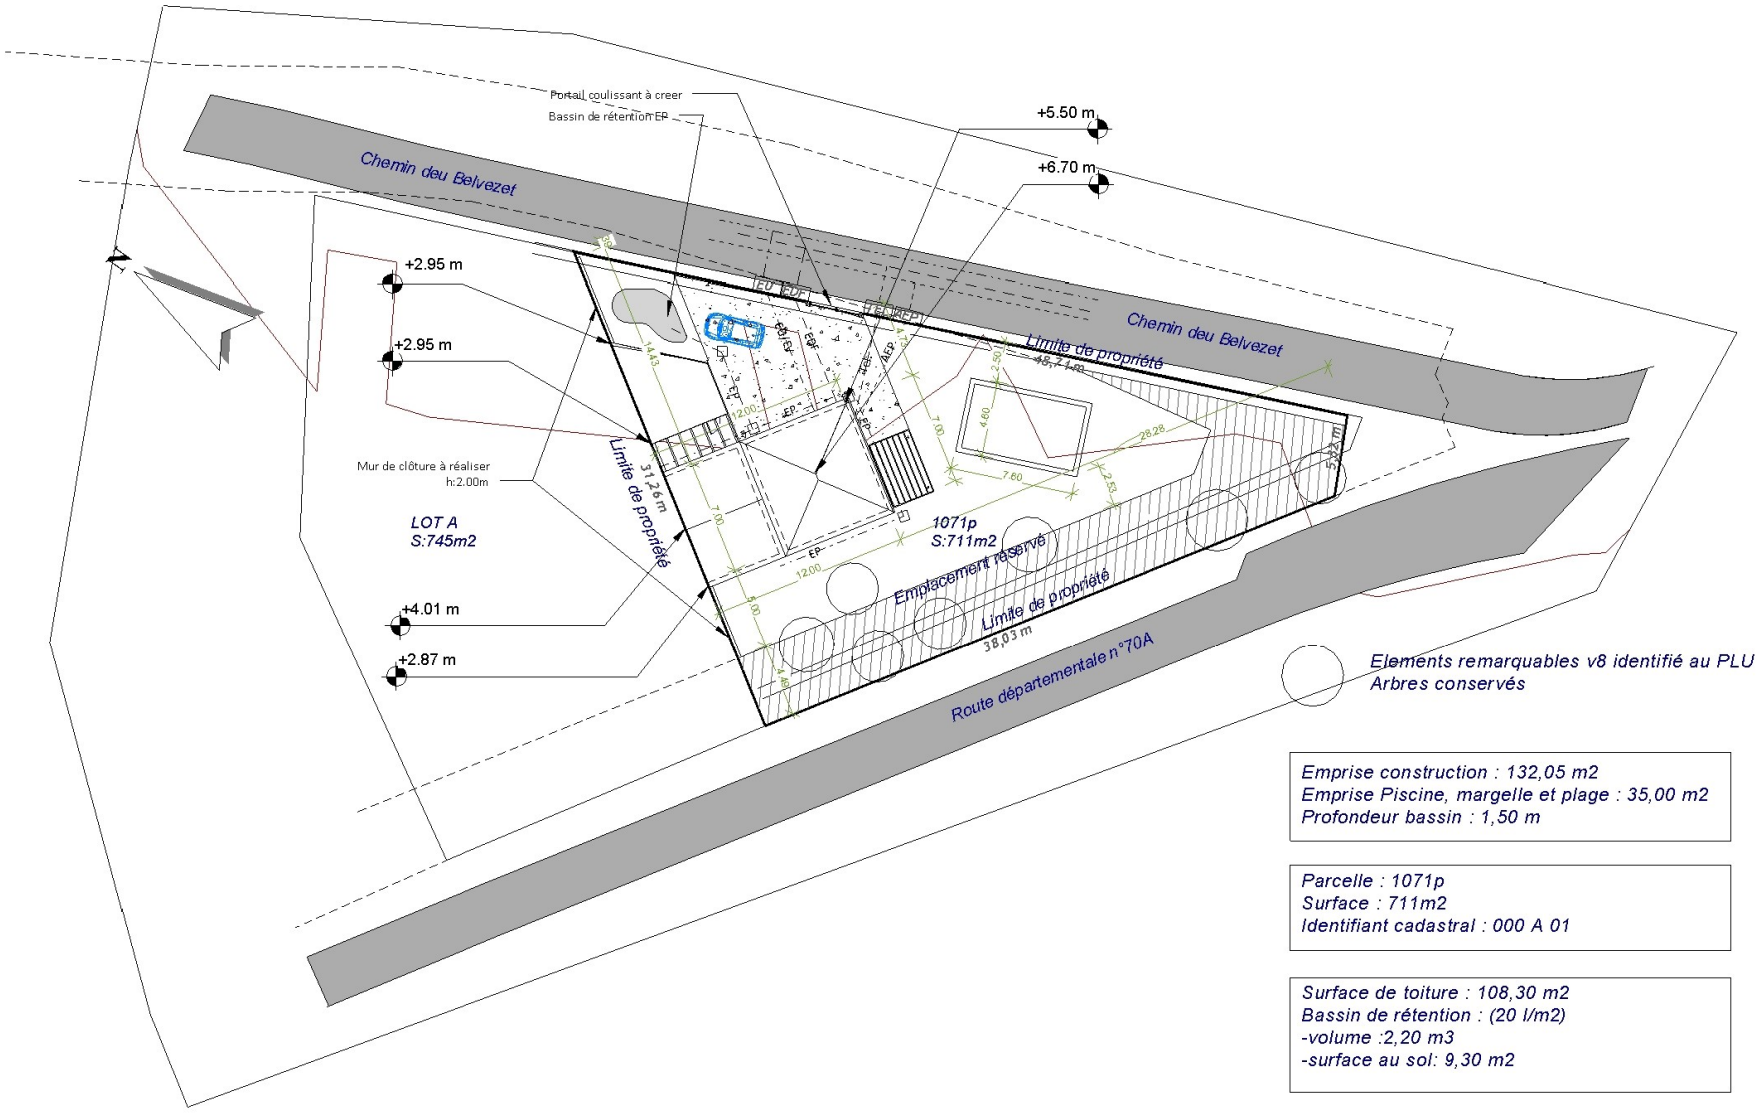

Emprise construction : 132,05 m2
Emprise Piscine, margelle et plage : 35,00 m2
Profondeur bassin : 1,50 m

Parcelle : 1071p
Surface : 711m2
Identifiant cadastral : 000 A 01

Surface de toiture : 108,30 m2
Bassin de rétention : (20 l/m2)
-volume :2,20 m3
-surface au sol: 9,30 m2

DPC

Réalisation d'une Maison individuelle

N°	Description	Date

Maître d'ouvrage
M.Bose
10, Rue Deners 31000 Toulouse
06.13.24.46.56
Projet :
12, chemin du Trigan
31300 Toulouse


PCMI 2

Numéro du projet	V1
Date	Juin 2016
Dessiné par	M.Architecte

Plan de Masse

Echelle 1 : 300

08/08/2016 11:24:14

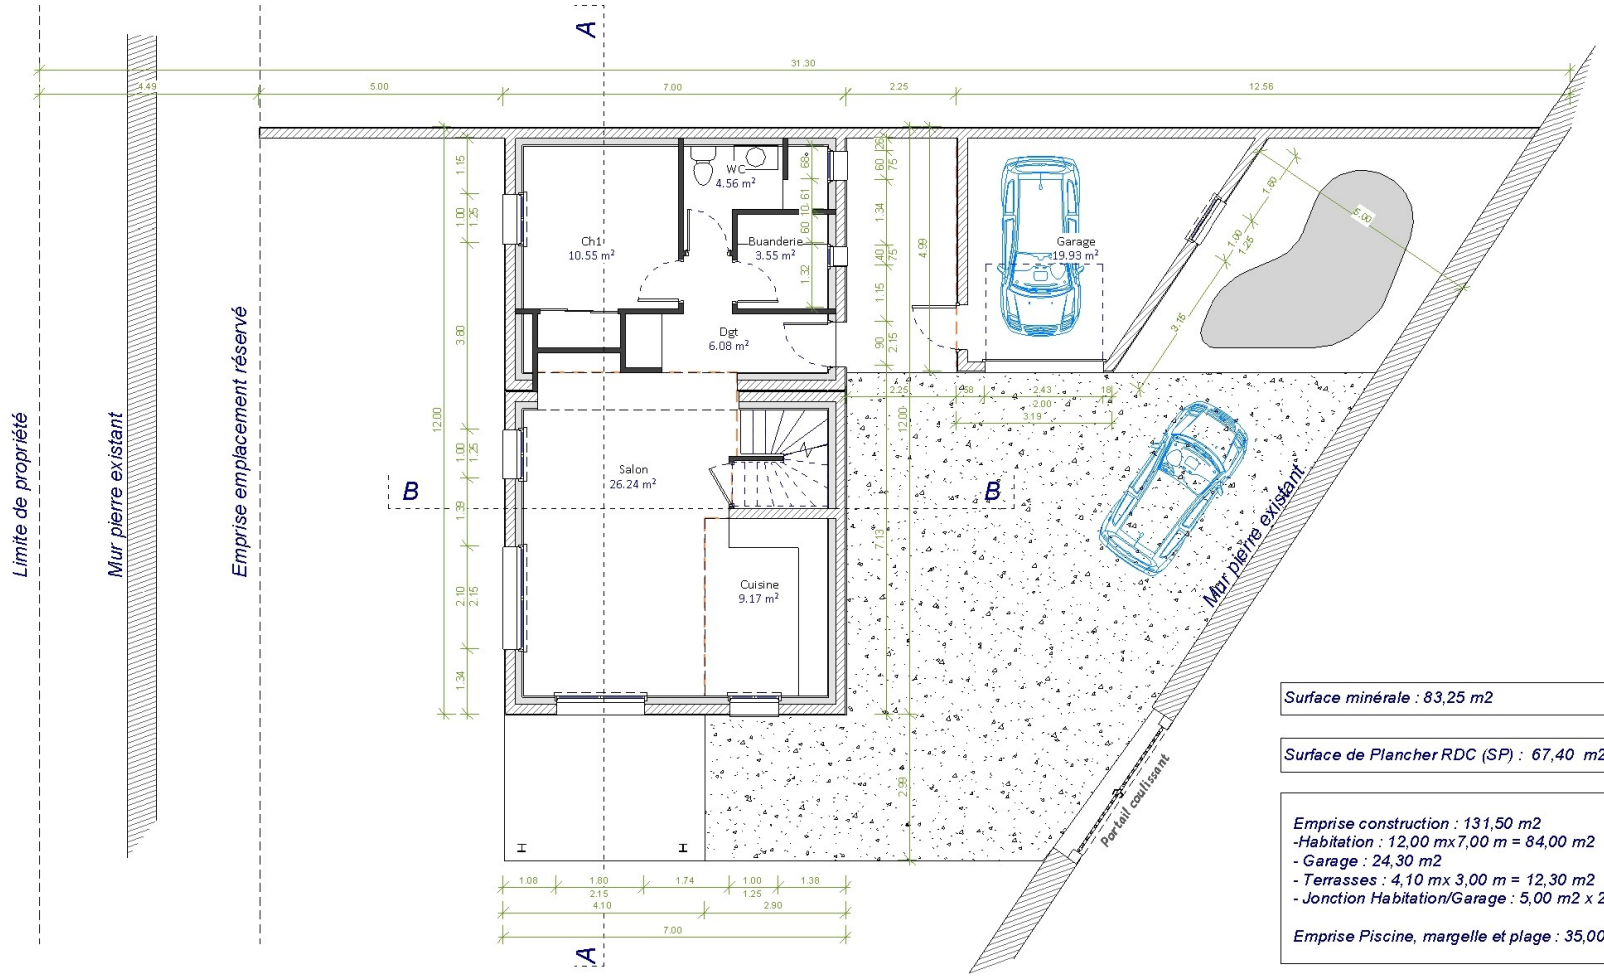

Surface minérale : 83,25 m2

Surface de Plancher RDC (SP) : 67,40 m2

Emprise construction : 131,50 m2
-Habitation : 12,00 mx7,00 m = 84,00 m2
- Garage : 24,30 m2
- Terrasses : 4,10 mx 3,00 m = 12,30 m2
- Jonction Habitation/Garage : 5,00 m2 x 2,25 m2 = 11,25m2

Emprise Piscine, margelle et plage : 35,00 m2

DPC

Réalisation d'une Maison individuelle

N°	Description	Date

Maître d'ouvrage
M.Bose
10, Rue Deners 31000 Toulouse
06.13.24.46.56
Projet :
12, chemin du Trigan
31300 Toulouse


PCMI

Numéro du projet	V1
Date	Juin 2016
Dessiné par	M.Architecte


PLAN RDC

Echelle 1 : 100

08/08/2016 11:25:57

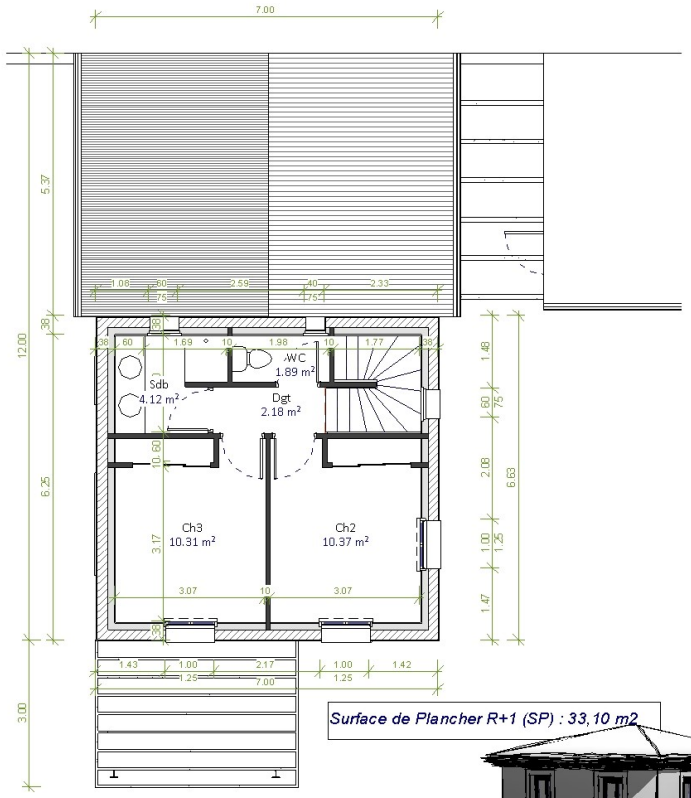

Surface de Plancher R+1 (SP) : 33,10 m2

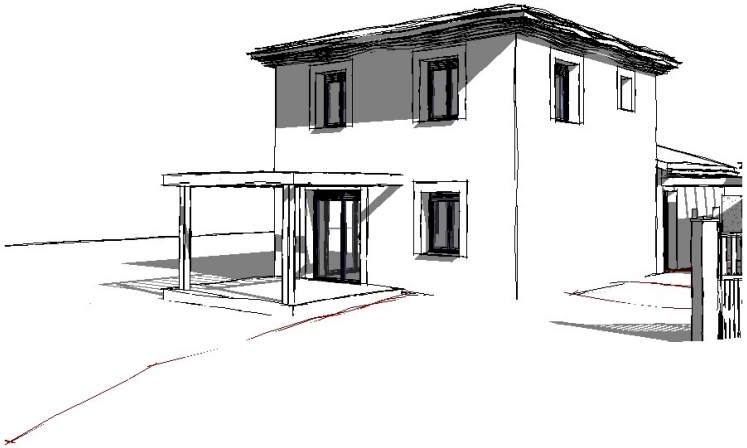





DPC	N°	Description	Date
Réalisation d'une Maison individuelle			

Maître d'ouvrage
M.Bose
10, Rue Deners 31000 Toulouse
06.13.24.46.56


Projet :
12, chemin du Trigan
31300 Toulouse

PCMI


Numéro du projet	V1
Date	Juin 2016
Dessiné par	M.Architecte
Echelle	1 : 100

PLAN ETAGE

08/08/2016 11:25:07

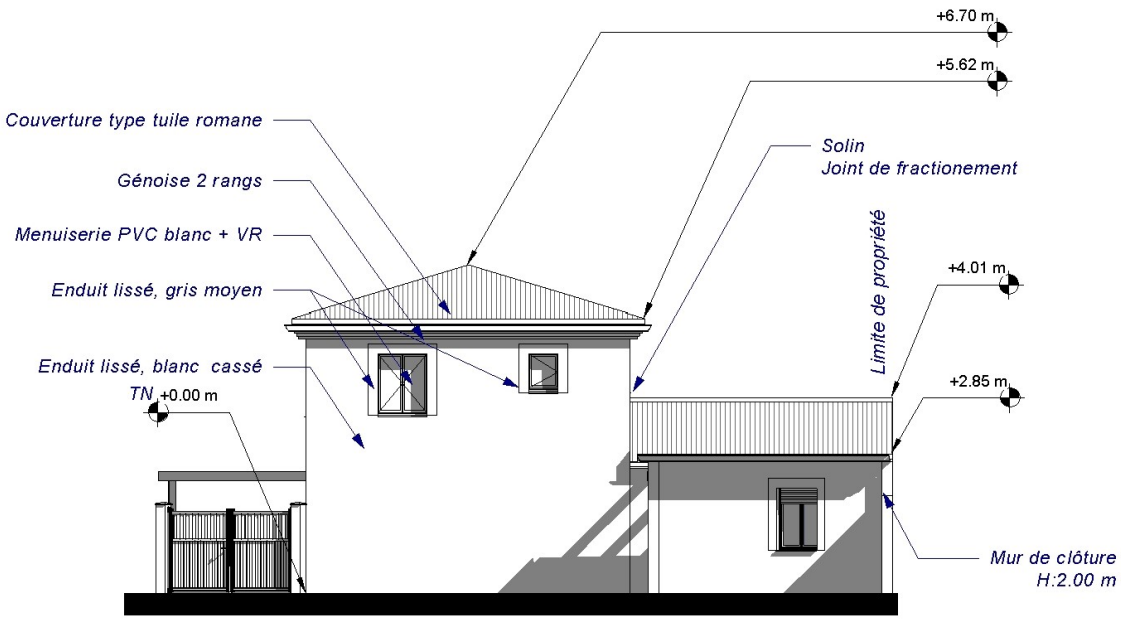

Façade Nord-Est

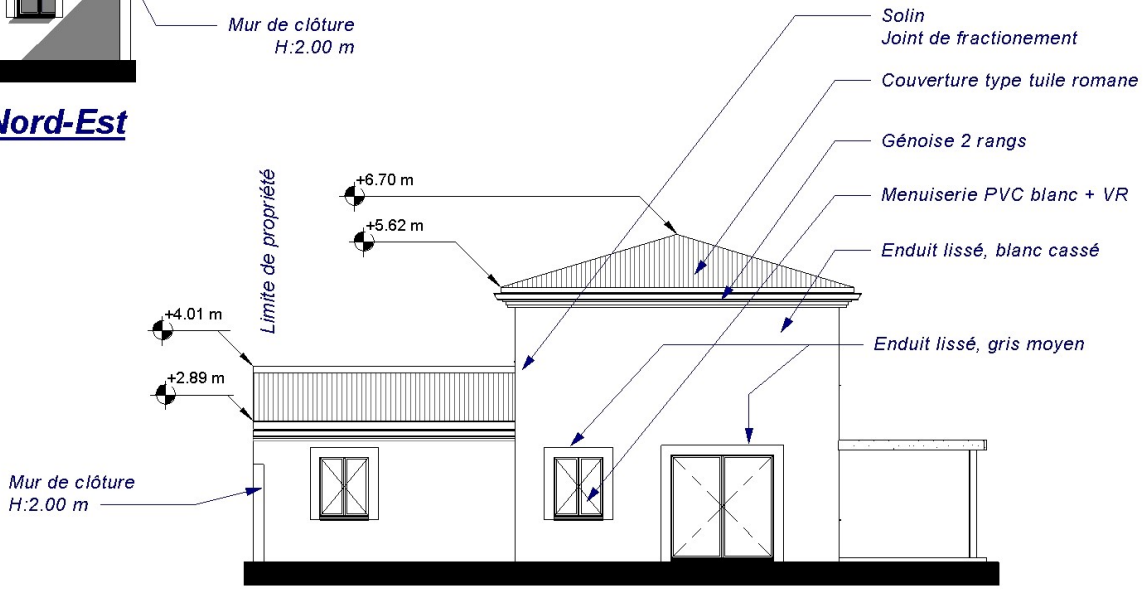

Façade Sud-Ouest

DPC

Réalisation d'une Maison individuelle

N°	Description	Date


Maître d'ouvrage
M.Bose
10, Rue Deners 31000 Toulouse
06.13.24.46.56
Projet :
12, chemin du Trigan
31300 Toulouse

PCMI5


Numéro du projet	V1
Date	Juin 2016
Dessiné par	M.Architecte
Echelle	1 : 100

Façade

08/08/2016 11:23:10

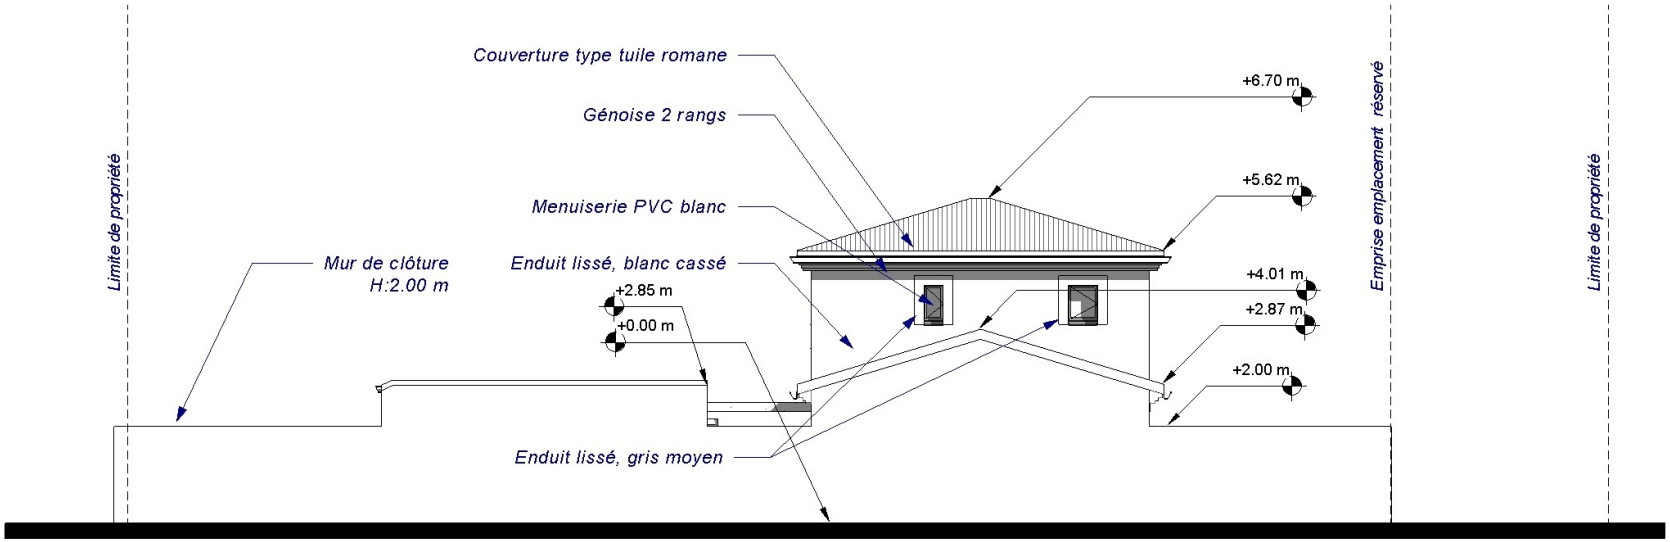

Façade Nord Ouest

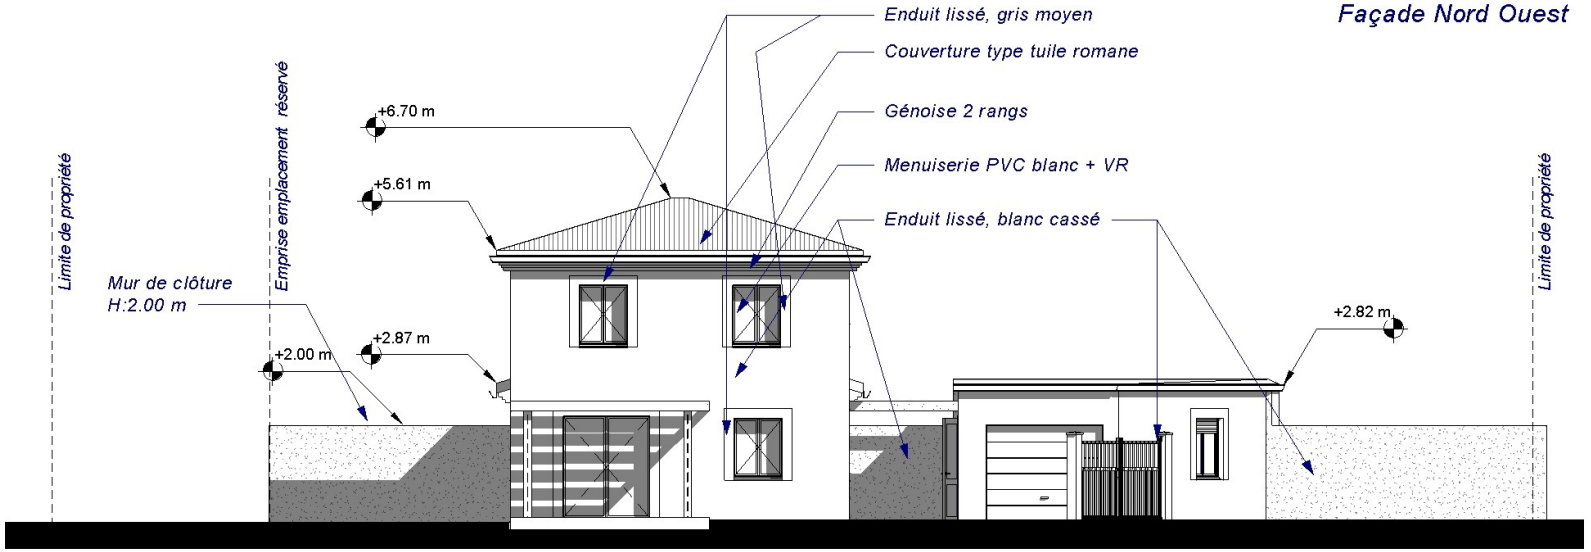

Façade Sud-Est

DPC

Réalisation d'une Maison individuelle

N°	Description	Date

Maître d'ouvrage
M.Bose
10, Rue Deners 31000 Toulouse
06.13.24.46.56
Projet :
12, chemin du Trigan
31300 Toulouse


PCMI 5

Numéro du projet	V1
Date	Juin 2016
Dessiné par	M.Architecte


Façades


Echelle 1 : 100

08/08/2016 11:23:31

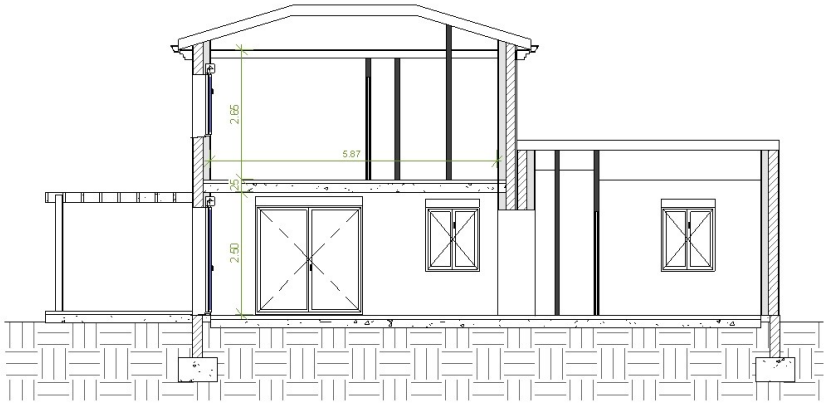

Coupe AA

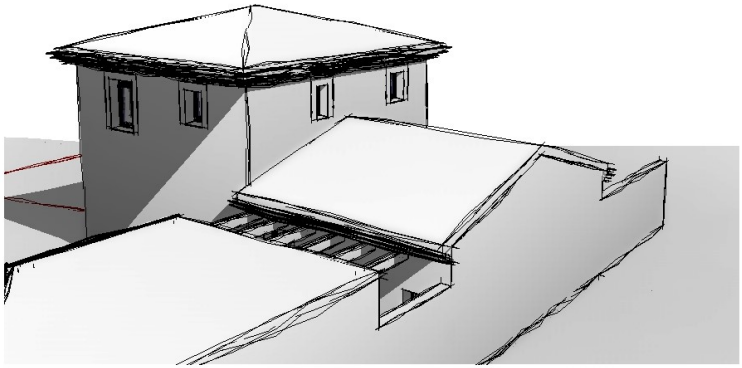

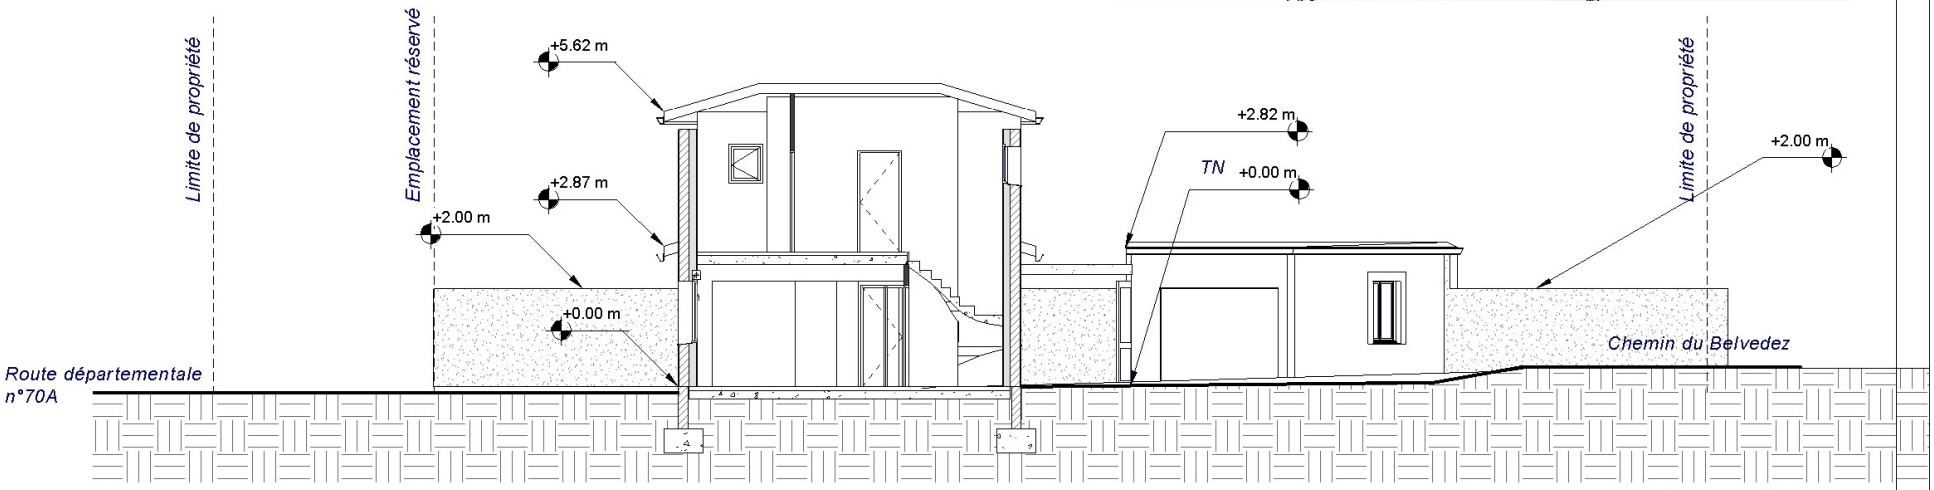

Coupe BB

DPC

Réalisation d'une Maison individuelle

N°	Description	Date

Maître d'ouvrage
M.Bose
10, Rue Deners 31000 Toulouse
06.13.24.46.56
Projet :
12, chemin du Trigan
31300 Toulouse

PCMI 3

Numéro du projet	V1
Date	Juin 2016
Dessiné par	M.Architecte
Echelle	1 : 100

Coupes


08/08/2016 11:22:48




PCMI 6



PCMI 8

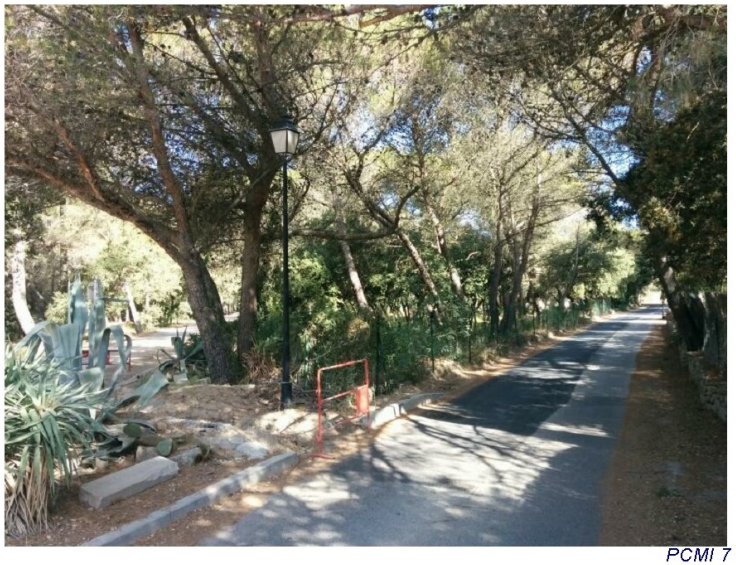

PCMI 7

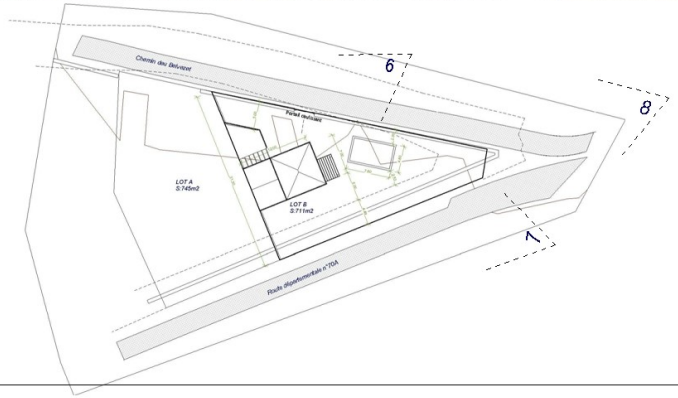

DPC

Réalisation d'une Maison individuelle

N°	Description	Date

Maître d'ouvrage
M.Bose
10, Rue Deners 31000 Toulouse
06.13.24.46.56
Projet :
12, chemin du Trigan
31300 Toulouse

PCMI 6, 7, 8

Numéro du projet	V1
Date	Juin 2016
Dessiné par	M.Architecte

Perspective

Echelle

08/08/2016 11:23:52